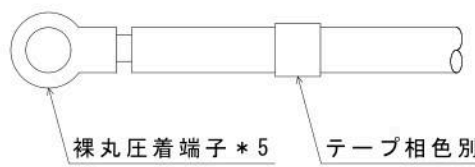
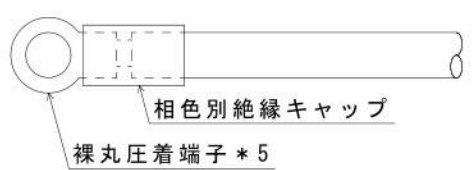
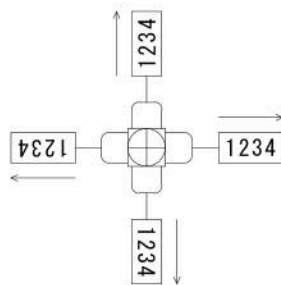



図面番号	図面名称	縮尺	用紙サイズ	備 考
E-01	製作仕様書	NS	A3 横	
E-02	継電器ユニット 複線接続図 1	NS	A3 横	
E-03	継電器ユニット 複線接続図 2	NS	A3 横	
E-04	継電器ユニット 機器配置図	1/4	A3 横	
E-05	単線結線図	NS	A1 横	
部品-00	部品明細表	NS	A3 横	継電器ユニット用
参考-01	Q B 内機器配置図	1/10	A3 横	

製作仕様書

使用電線・電線色・電線の太さ	* 1	高 圧	主 回 路		KIP（高圧WL含む）又は　銅 帯		
			分　岐		KIP（高圧WL含む）		
			V T－時側		KIP（高圧WL含む）14 [□]		
			L A 高圧側		KIP（高圧WL含む）14 [□]		
	低 圧	主　回　路 （交流）		IV黄（WL黒含む）又は　銅 帯 HIV黄（非常電源回路　又は　その制御）			
		主　回　路 （直流）		IV黄（WL黒含む）又は　銅 帯 HIV黄（非常電源回路　又は　その制御）			
	そ の 他 * 3	交流制御回路		IV1.25 [□] 黄（* 2）			
		直流制御回路		IV1.25 [□] 黄（* 2）			
		接地線		IV線（* 1）			
		接地母線		銅 帯 メ ッ キ			
		V T 二 次		IV2 [□] 黄、VCTF			
		C T 二 次		IV2 [□] 黄、VCTF			
	注）* 1　電線の太さは各負荷容量に依ります。 * 2　電線の太さは各負荷容量に依り、IV2 [□] を使用します。 * 3　【エコ電線（EM電線）も使用します】 他、図面内記入電線種及びサイズとします。						
	銅 帯 処 理	表　　面		メ ッ キ			
色　　別		シ ー ル					
被　　覆		無					
端 末 の 相 色 別	交 流	相 別 / 線 方 式	3 φ 4W	3 φ 3W		1 φ 3W	1 φ 2W
				400V級	高 圧 200V級		
		第一相	赤	赤	赤	赤	* 4
		第二相	黒	黒	白	黒	* 4
		第三相	青	青	青	—	—
		中性相	白	—	—	白	—
	直 流	正 極 側		赤			
		負 極 側		青			
	注）* 4　分岐前の相色別とします。						

配線仕様	端 末 処 理	高 圧 主 回 路		
		低 圧 主 回 路		
		制 御 回 路	圧 着 端 子	フ ォ ー ク 型
				
マ ー ク チ ュ ー プ 挿 入 方 向	標 準	注）* 5　機器端子の形状によっては 機器メーカー推奨の端末処理とします。 * 6　器具の端子が平ワッシャの場合は 丸形を使用します。		
				



押 釦 ・ 表 示 灯 色	用　途	押　釦	表　示　灯
	電　源		白
	入・運転	赤	赤
	切・停止	緑	緑
	非常停止	赤	
	警　報		橙
	リセット	黄	
	ランプテスト	黄	
	ブザー停止	黒	
一 般 仕 様	盤の保護構造・使用材料・塗装色は 各盤の外形図に指示します。 盤内部にZAM材（溶融亜鉛ーアルミニウムーマグネシウム） 合金めっき鋼板）を使用する場合、ZAM材は塗装無しとします。		
	1．準拠規格 日本電機工業会規格　　　　　（J E M） 日本産業規格　　　　　　　　（J I S） 電気規格調査会標準規格　　（J E C） 日本電気協会標準資料　　（J E A C） 2．保証 御客先引渡後１年以内に弊社の 設計、製作及び材料の不良に 基く事故または不具合が生じた場合は 無償にて修理または交換を行います。		
銘 板	材質・構造	透明アクリル	
	文　　字	丸ゴシック体、白地黒文字	
	寸　法		用途
	63×315×5t 40×200×3t 30×150×3t		盤 名 称 銘 板
	16×　50×2t		
	10×　40×2t		
	他図面記入寸法とします。		そ の 他

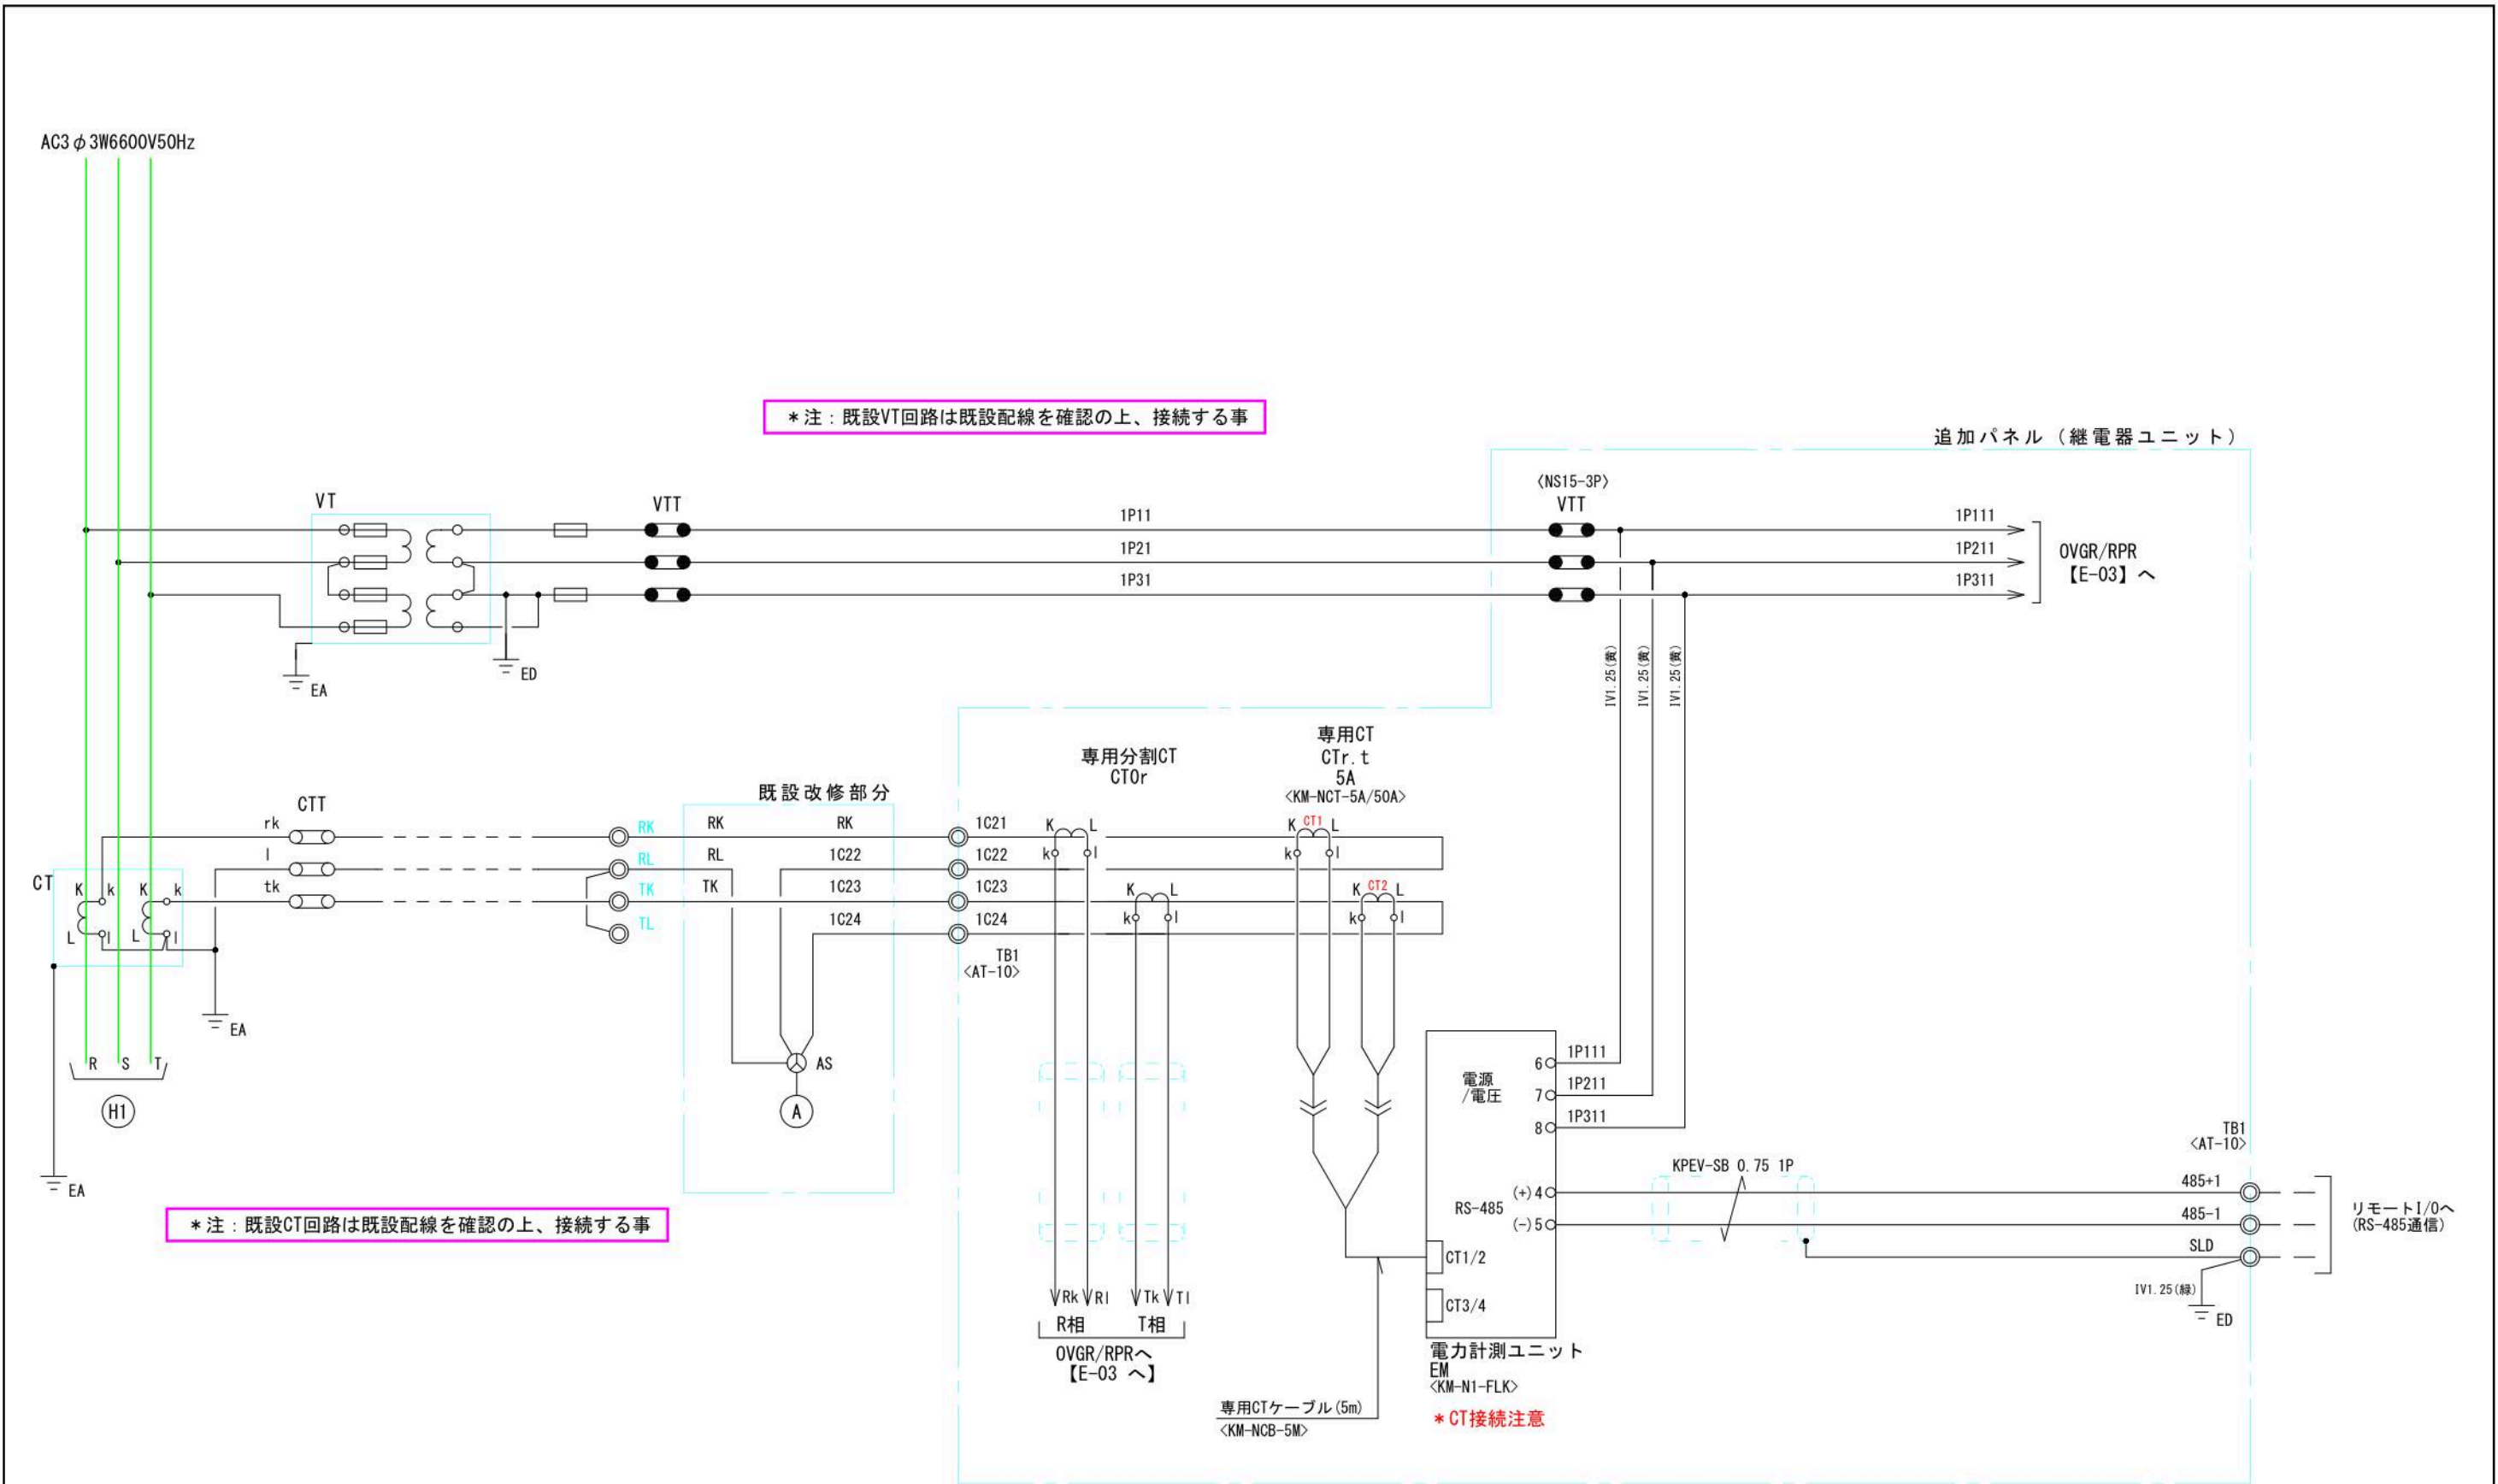

受電VT・CT回路
参考図

<凡例及び特記事項>		承認	検 査	設 計	日 付	工事名称	No.
	本社				2024/8/22-②	(株) 2段階連携型太陽光発電設備工事	E-02
					Scale (A3) S=N	継電器ユニット 複線接続図1	

設置場所	屋内
設置方法	壁掛
構 造	-----
基 板	ZAM t1.6
塗装色	未塗装処理
製作数	1面

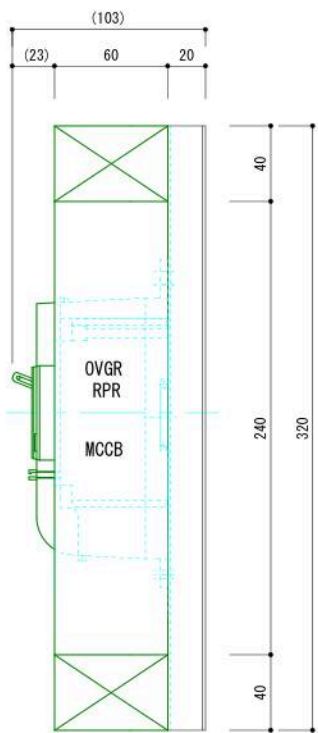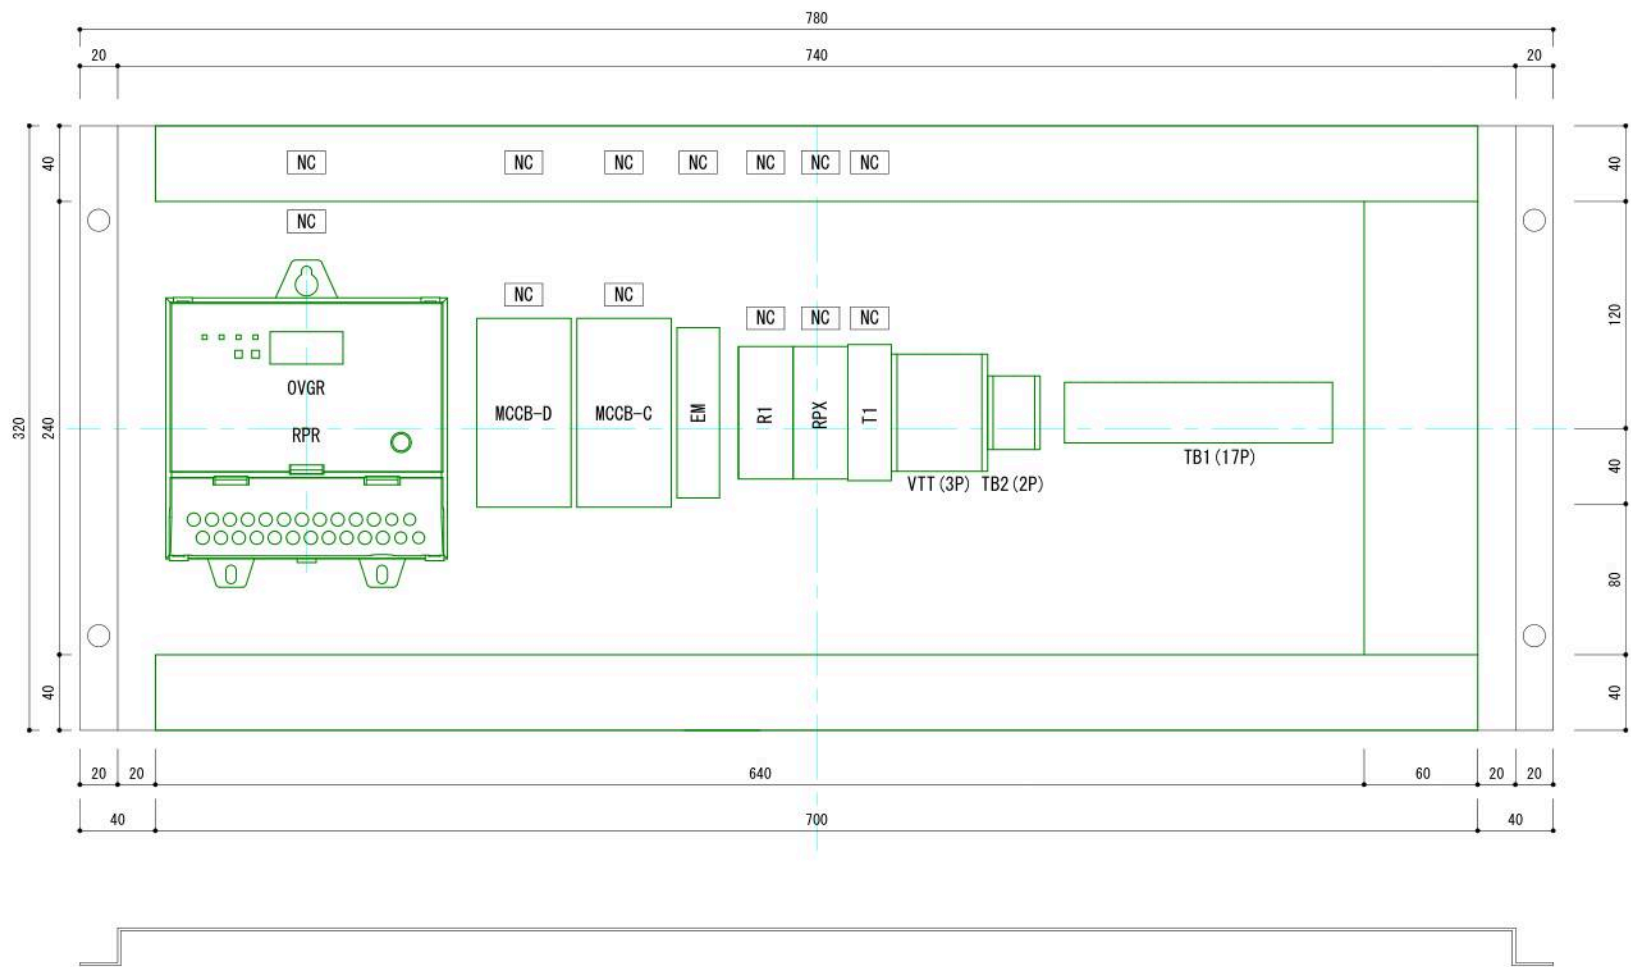


* 盤内零相碍子付近へ設置
零相電圧変換器



NC * テブラにて機器名称表示

端子台配列

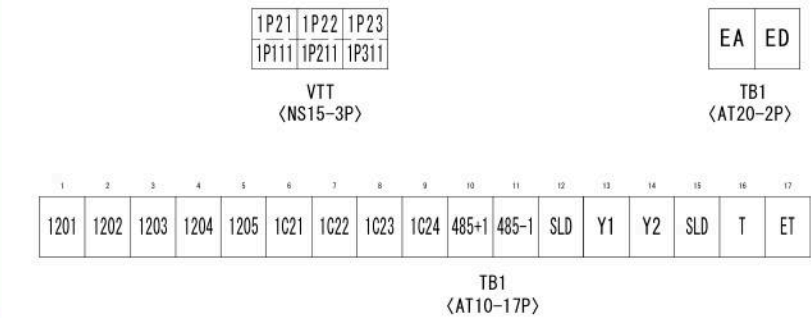

<凡例及び特記事項>



本社

承認

検図

設計

日付

2024/8/20

工事名称

2段階連携型太陽光発電設備工事


図面名

継電器ユニット 機器配置図


No.

E-04

低圧電灯盤内 機器配置図

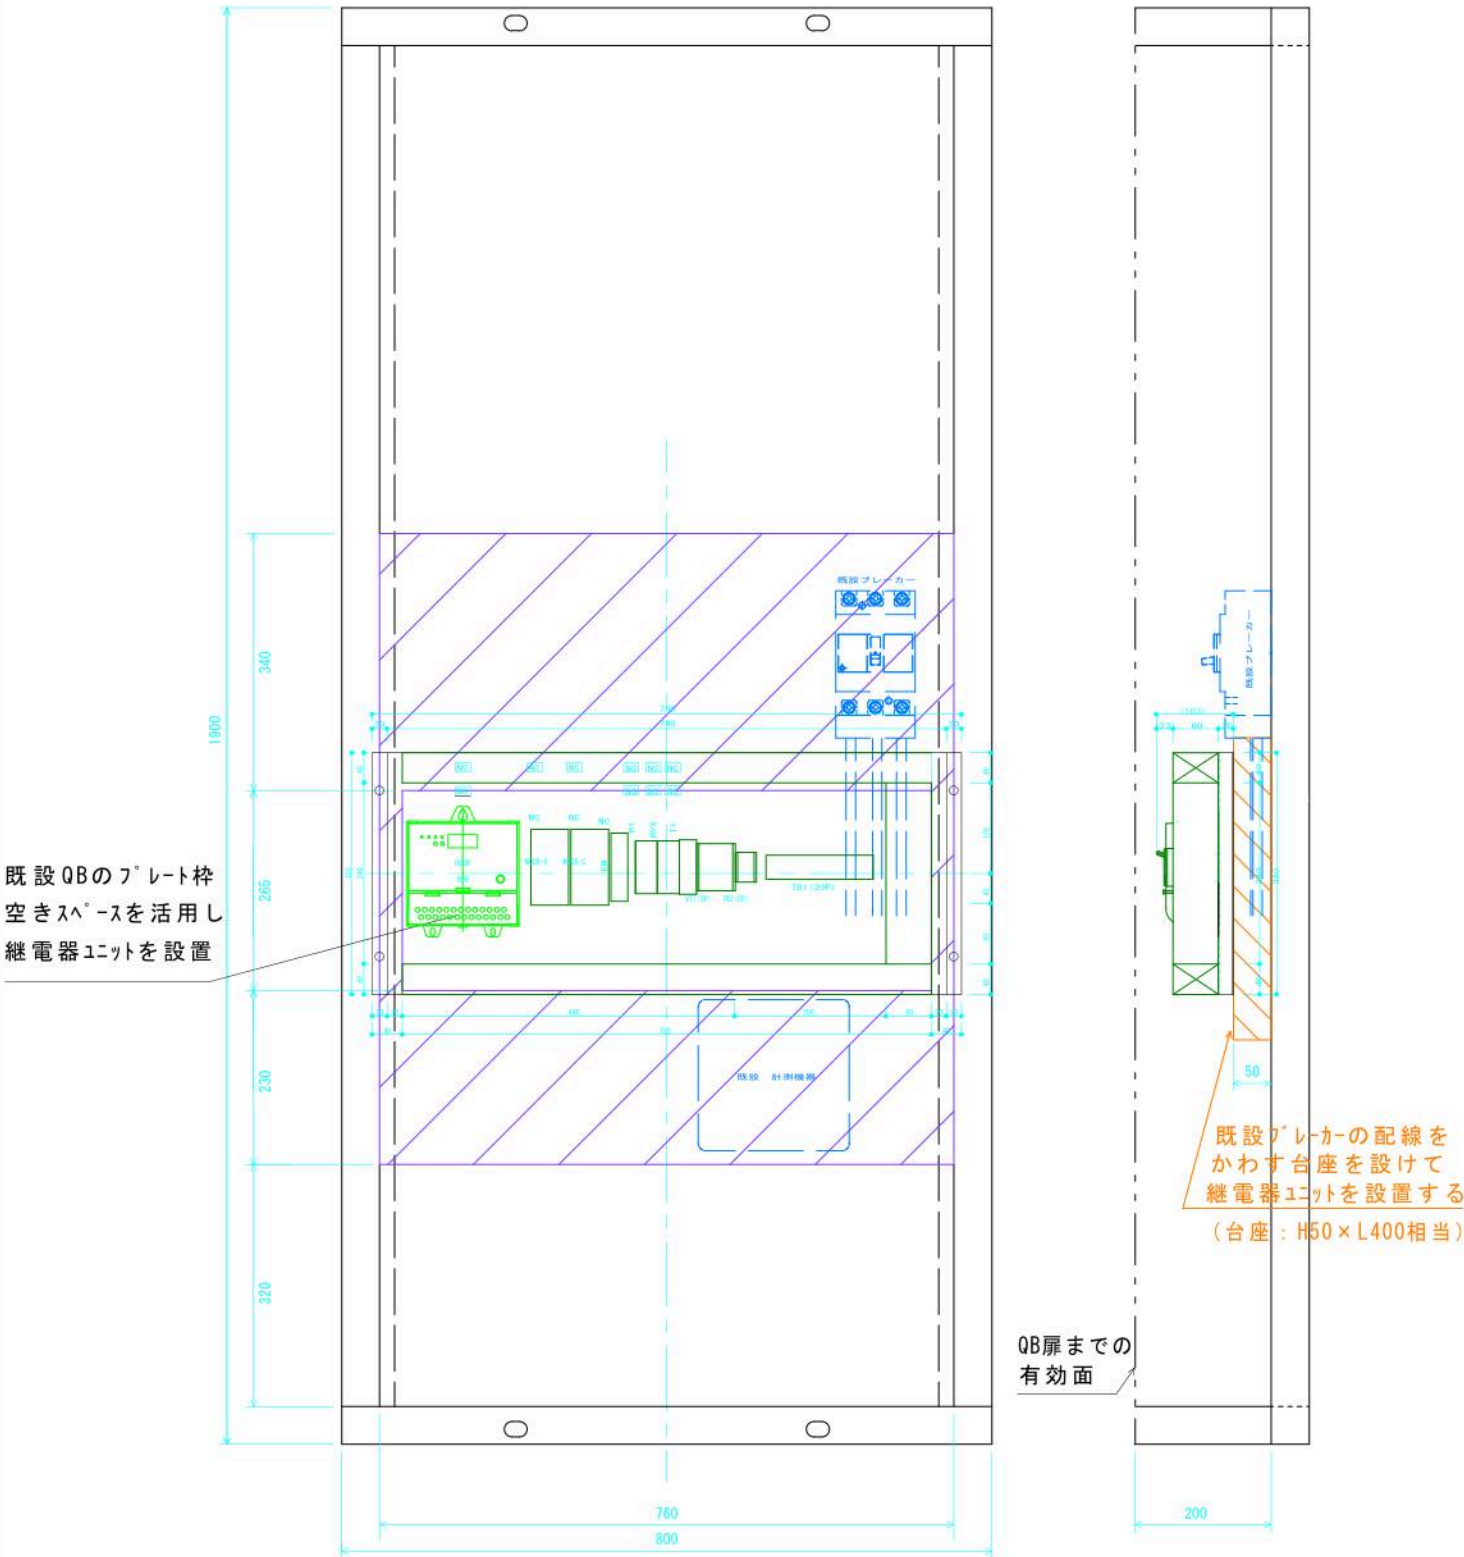

高圧動力盤内 機器配置図

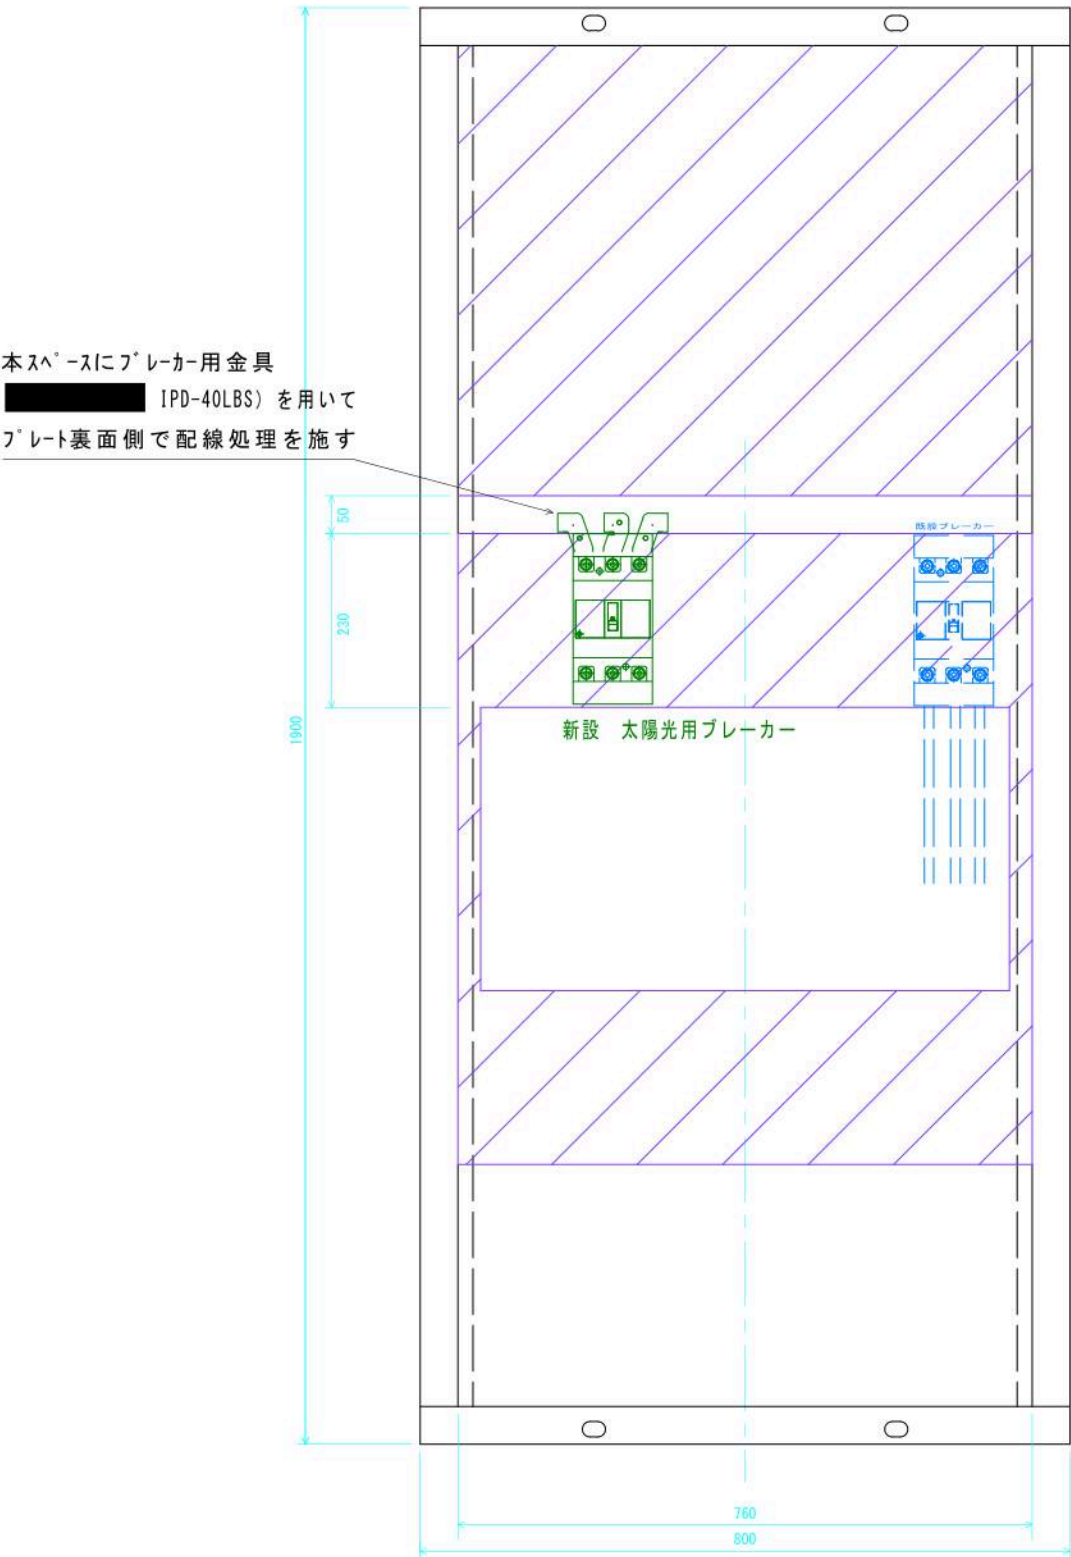

<凡例及び特記事項>



本社

承認

検図

設計

日付

2024/8/20

Scale

(A3) S=1/10

工事名称

(株)イ
2段階連携型太陽光発電設備工事

図面名

QB内機器配置図 (継電器ユニット、ブレーカー配置)

No.

参-01

部品明細表

* 区分	
0=支給品無	1=無償支給
2=有償支給	3=先行手配

行No.	部品記号	部 品 名	型 式	仕 様 (1)	仕 様 (2)	メーカー名	数 量	区 分
1	〈継電器パネル〉	*	*			*		0
2	OVGR (64R)+RPR (67P)	完全自家消費専用保護継電器 (OVGR/RPR)	形KP-PRRV-CPC	定格電圧AC/DC110V 表面取付型 停電補償時間 最大3秒	専用CT同梱	■■■■■	1	0 T
3	ZPD-C. T	零相電圧検出装置	形VOC-1MS2	250pF×3	リード線1.0m セット型番	■■■■■	1	0 T
4	*	CT二次接続電線	*	MVVS 0.75mm2 1芯シールド線 L=1m		■■■■■	1	0
5	MCCB-D	配線用遮断器	BW50SAG	2P 20AT	端子カバー (BW9BTAA-S2W) 付	■■■■■	1	3
6	MCCB-C	配線用遮断器	BW50EAG	2P 5AT	端子カバー (BW9BTAA-S2W) 付	■■■■■	1	3
7	R1, RPX	リレー	RU4S-C-A100	AC100Vコイル 4C	ソケット (RU4S-05DN) 付 金具 (SFA-502) 付	■■■■■	2	3
8	T1	オンディレータイマー	H3Y-2	AC100V 0.5min-10min	ソケット (PYFZ-08), 金具 (Y92H-3) 付	■■■■■	1	3
9	TB1	端子台 (17P)	AT-10	600V 20A 2sq M3.5		■■■■■	17	3
10	TB2	端子台 (2P)	AT-20	600V 40A 5.5sq M4		■■■■■	2	3
11	VTT	断路端子台 (3P)	NS-15	定格電流 600V 15A M4	適合電線1.25~5.5mm ²	■■■■■	3	3
12	*	端子台側板	NSE-15	NS-15用		不二電機 ■■■■■	2	3
13	〈支給品〉	*	*			*		0
14	EM	小型電力量モニタ	KM-N1-FLK	電源電圧 AC100-240V	端子カバー付	オムロン ■■■■■	1	1
15	CTr. t	分割型変流器	KM-NCT-5A/50A	定格一次側電流 5A/50A	KM-N1専用	オムロン ■■■■■	2	1 付属品
16	*	専用CT用ケーブル	KM-NCB-5M	5m		オムロン ■■■■■	1	1 付属品
17								
18								
19								
20								
20								

< 凡例及び特記事項 >



■■■■■
本社 ■■■■■

承 認	検 図	設 計	日 付	工事名称	No.
	■■■■■	■■■■■	2024/8/20	2段階連携型太陽光発電設備工事	部-00
			Scale (A3) S=N	図 面 名 部品明細表	