

[モジュール]

[モジュール]	
TMS-425DE09R	[Voc: 50.2V]
単結晶	425W
1762mm × 1134mm × 30mm	

[パワーコンディショナ]

[パワーコンディショナ]	
EPG-T99P5	
3φ3W 202V 9.9kW	自立運転機能付
W810.2mm × H563.1mm × D242.2mm	53kg

[モジュール設置容量]

425W × 372枚 = 158.1kW


[パワーコンディショナ設置容量]

9.9kW × 10台 = 99kW

[過積載率]

158.1kW ÷ 99kW = 159.69%

No.	容量	枚数	PCS1台当たりのモジュール合計容量
PCS 1	9.9kW	7直×3並=21枚 8直×2並=16枚 計 37枚	425W×37枚= 15.725kW
PCS 2	9.9kW	7直×3並=21枚 8直×2並=16枚 計 37枚	425W×37枚= 15.725kW
PCS 3	9.9kW	7直×3並=21枚 8直×2並=16枚 計 37枚	425W×37枚= 15.725kW
PCS 4	9.9kW	7直×3並=21枚 8直×2並=16枚 計 37枚	425W×37枚= 15.725kW
PCS 5	9.9kW	7直×3並=21枚 8直×2並=16枚 計 37枚	425W×37枚= 15.725kW
PCS 6	9.9kW	7直×3並=21枚 8直×2並=16枚 計 37枚	425W×37枚= 15.725kW
PCS 7	9.9kW	7直×3並=21枚 8直×2並=16枚 計 37枚	425W×37枚= 15.725kW
PCS 8	9.9kW	7直×3並=21枚 8直×2並=16枚 計 37枚	425W×37枚= 15.725kW
PCS 9	9.9kW	7直×2並=14枚 8直×3並=24枚 計 38枚	425W×38枚= 16.15kW
PCS10	9.9kW	7直×2並=14枚 8直×3並=24枚 計 38枚	425W×38枚= 16.15kW
合計10台	99kW	7直×28並=196枚 8直×22並=176枚 計372枚	425W×372枚= 158.1kW

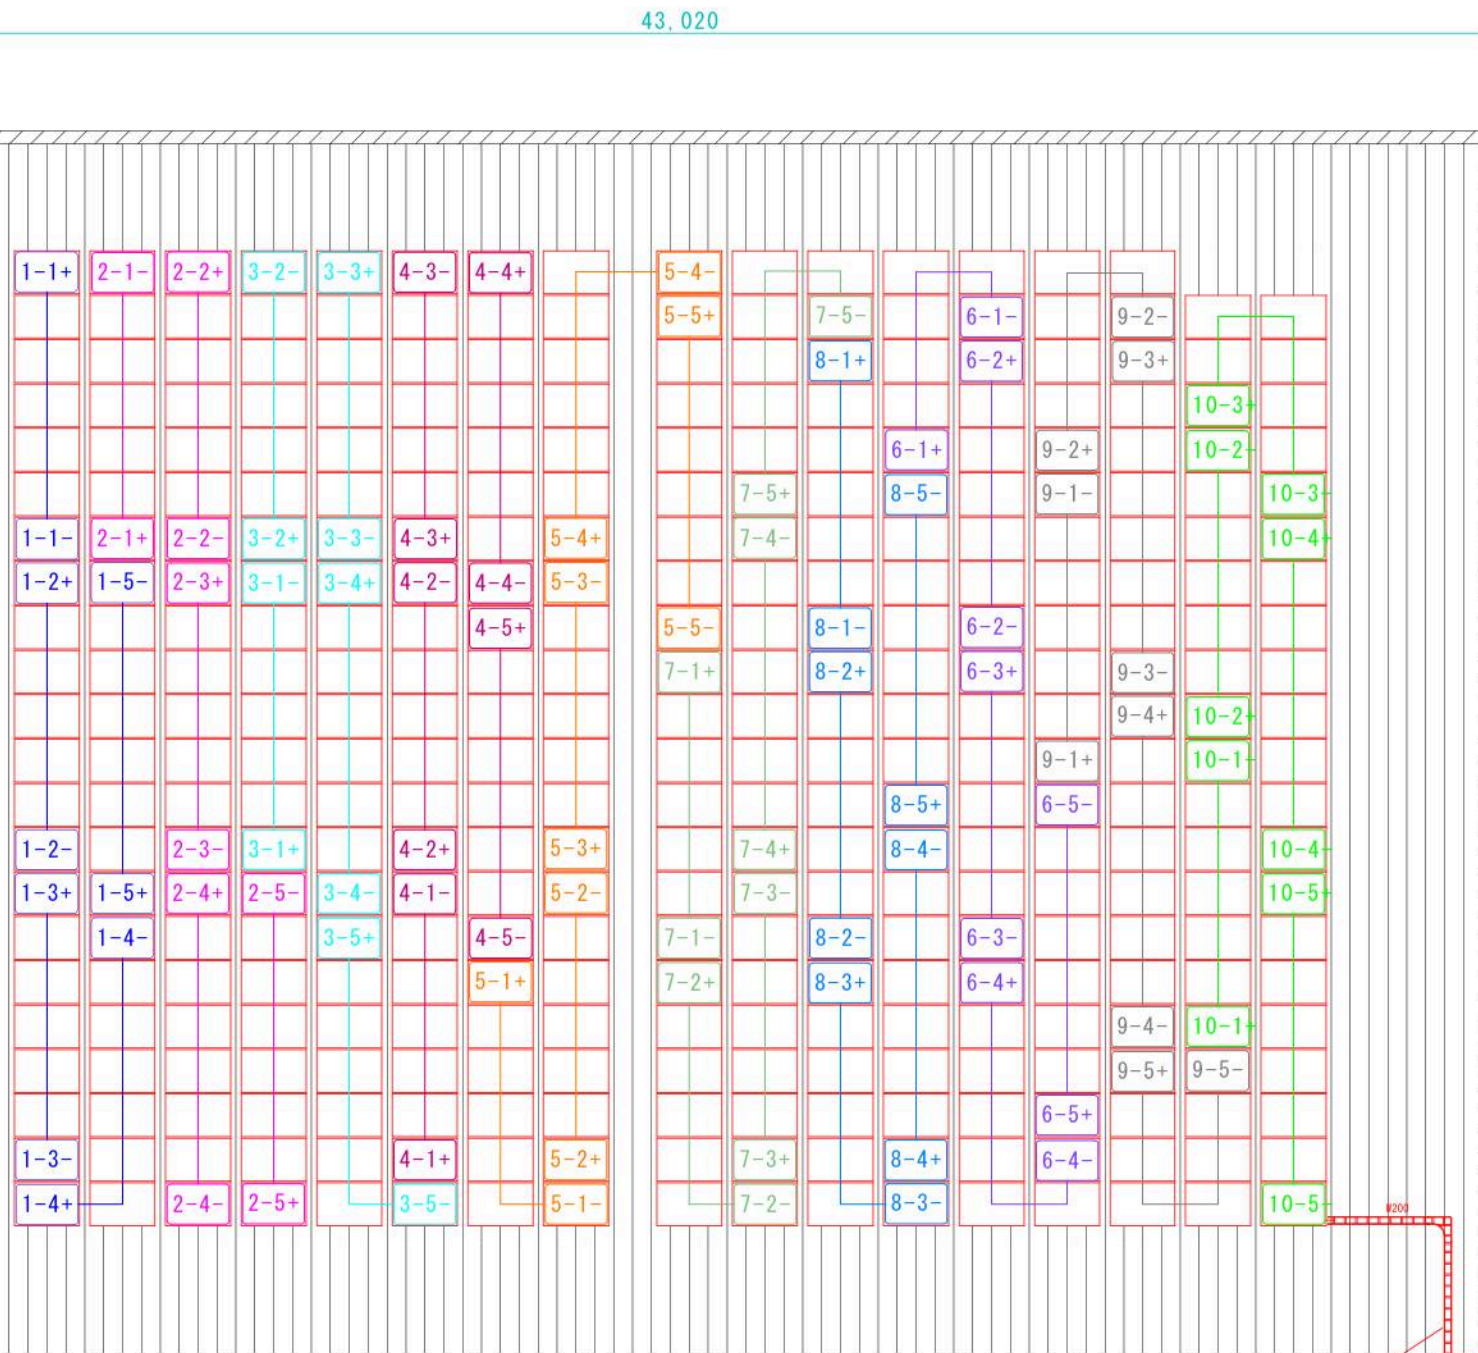

ケーブルラック壁付け

PCS×10台 (自立用1台)


監視装置・マスターボックス
自立コンセント

集電盤

既存ダクトに幹線等入れ込み

配管立下げ位置

既存キュービクル
・動力TR300kVA*2台

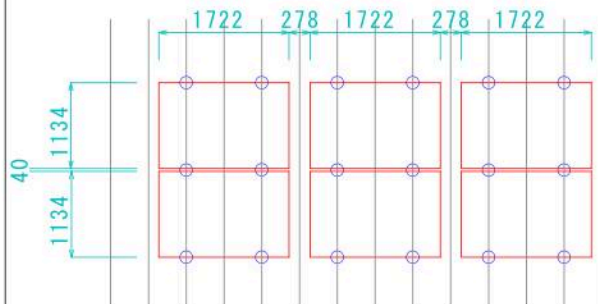

モジュール取り付け詳細図

< 凡例及び特記事項 > ※モジュールに影の影響が無い為、日影を記していません。 ※太陽電池モジュールの配置は端部より3m以上となります。		承認 検 査 設 計 日 付 2023/6/21 Scale (A3) S=1/200	工事名称 発電設備工事 図 面 名 モジュールストリング図面	No.	E-05