


ルなし)
ます。

作業日時	8月 4日(日) 9:00~12:00
搬入	太陽光モジュール×13パレット 掴み金具×1パレット、電材等
搬入車両	10tトラック平車×2台
仕様重機	25tラフタークレーン

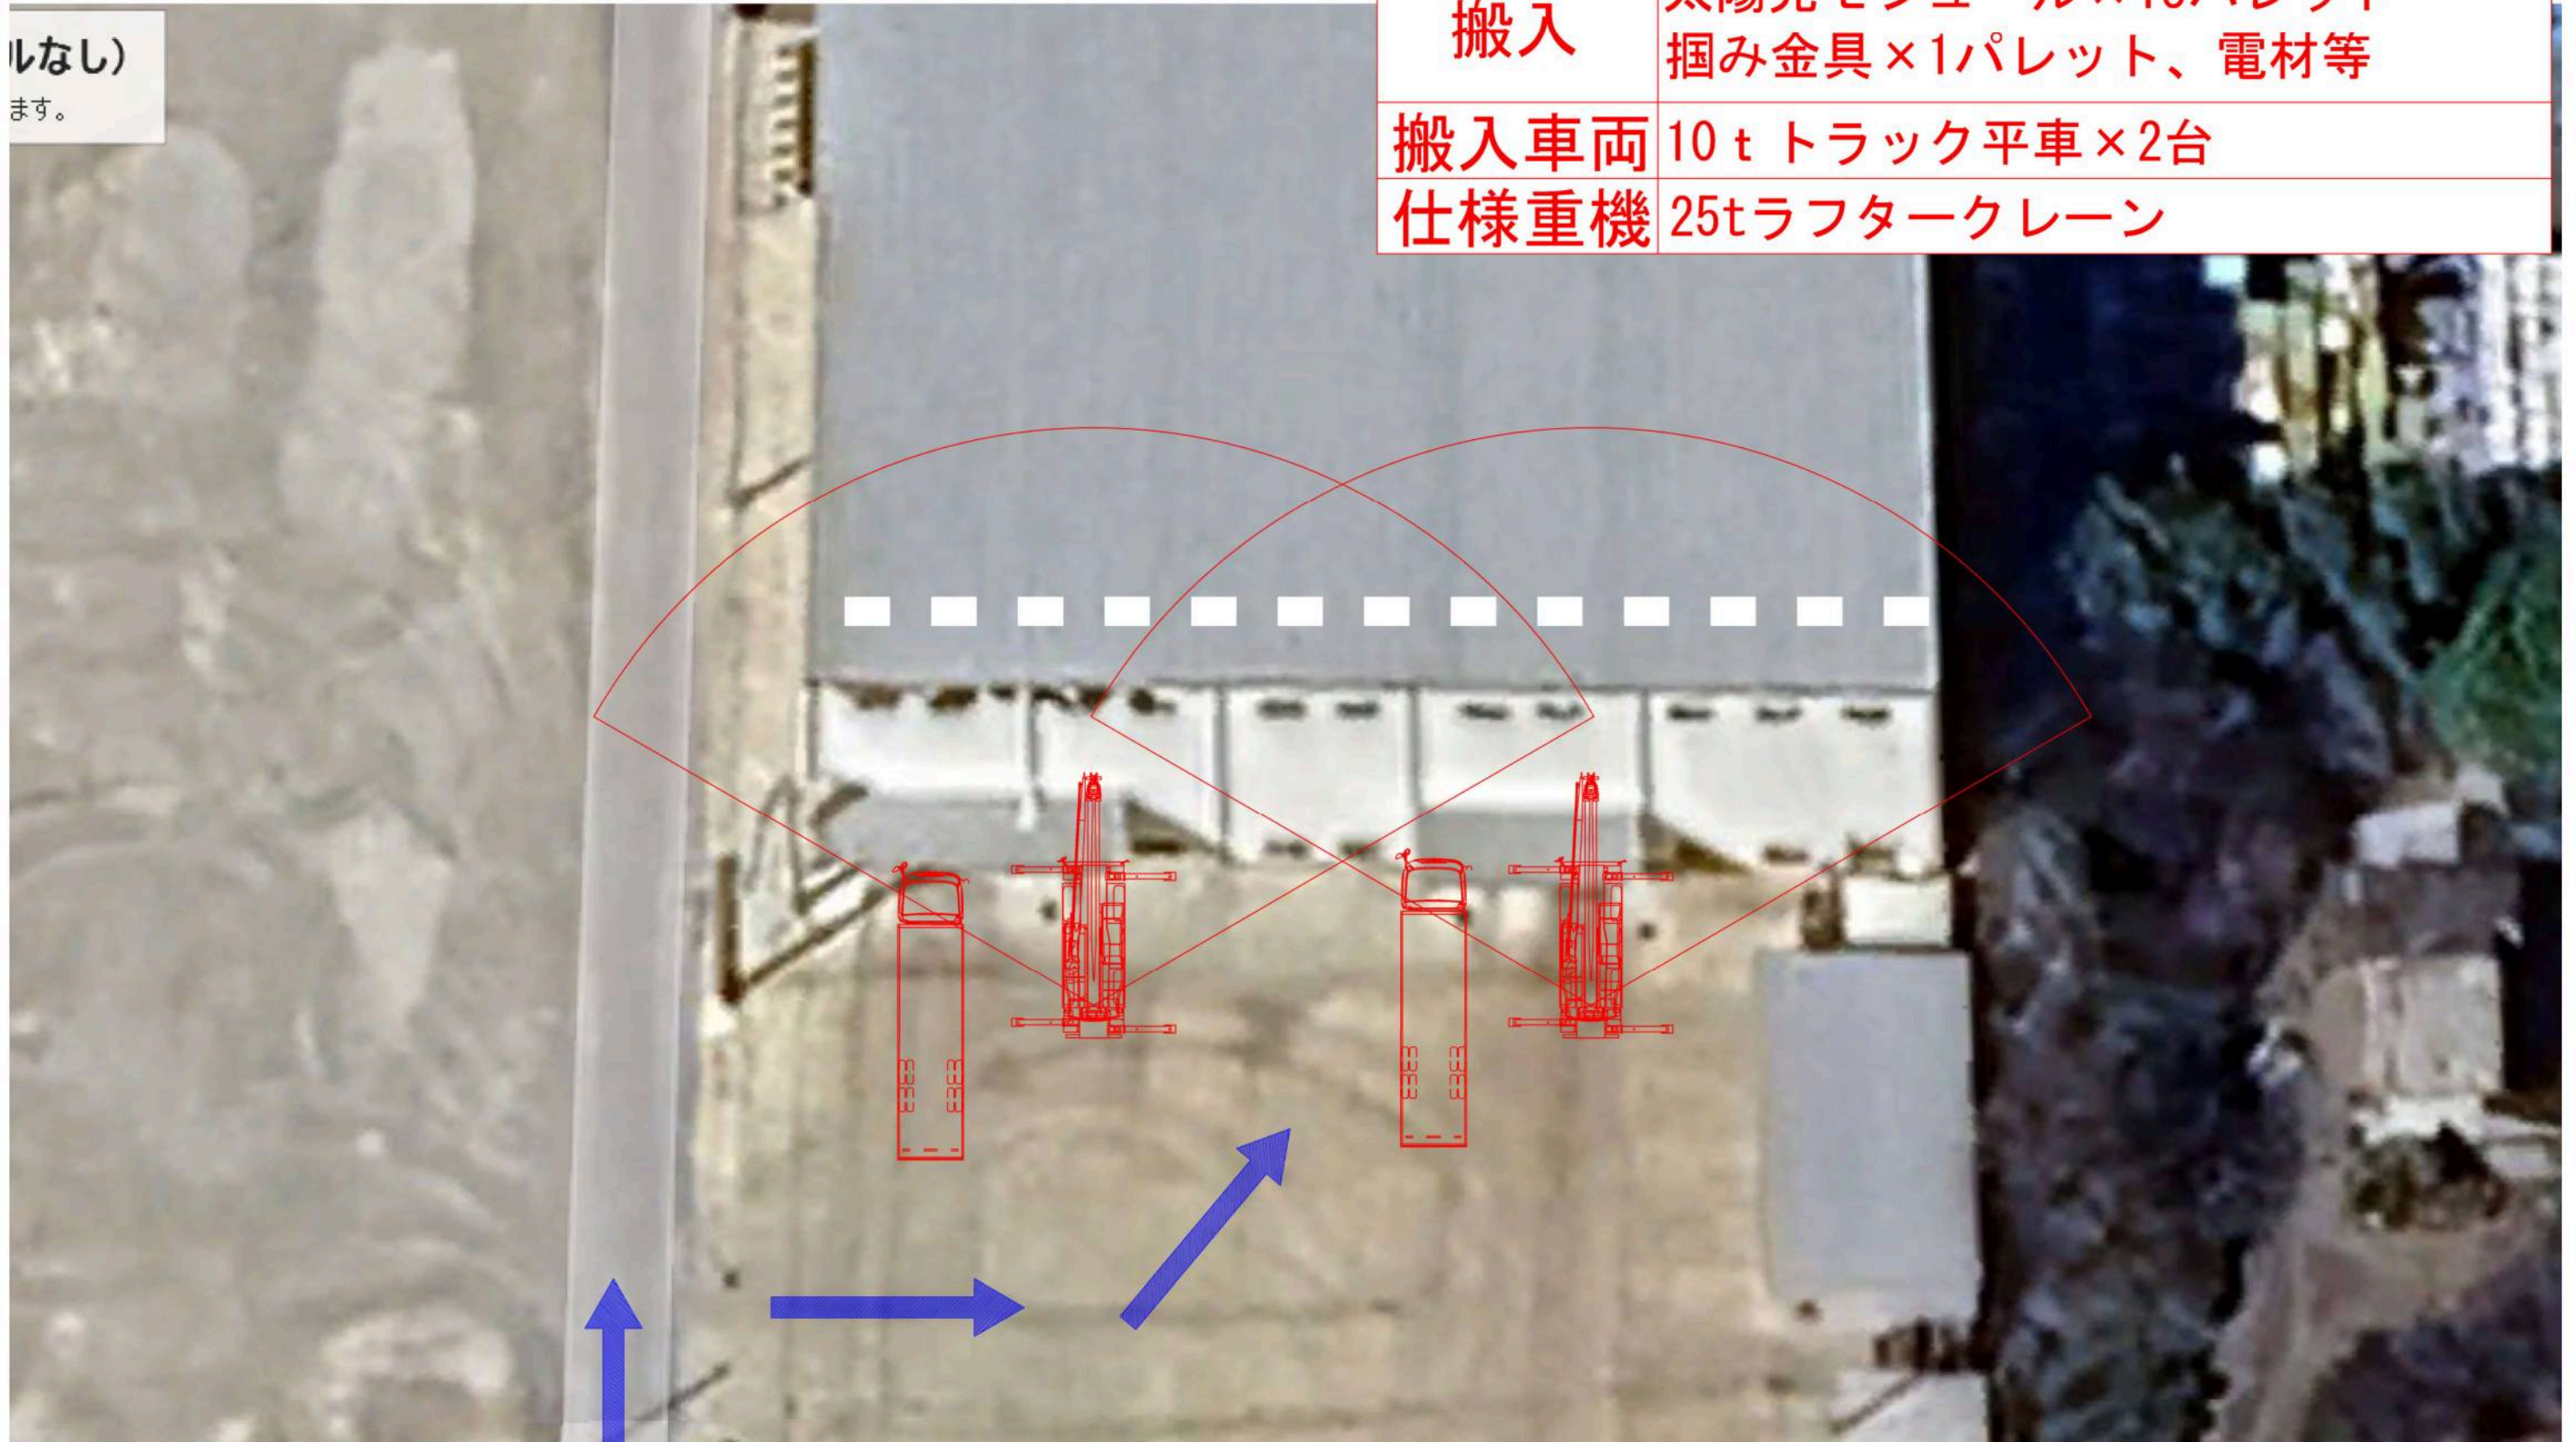

<凡例及び特記事項>	本社	承認	検図	設計	日付	工事名称	No.
					2023/6/21	太陽光発電設備工事	
					Scale	図面名	
					(A3) S=1/250	搬入計画図	