


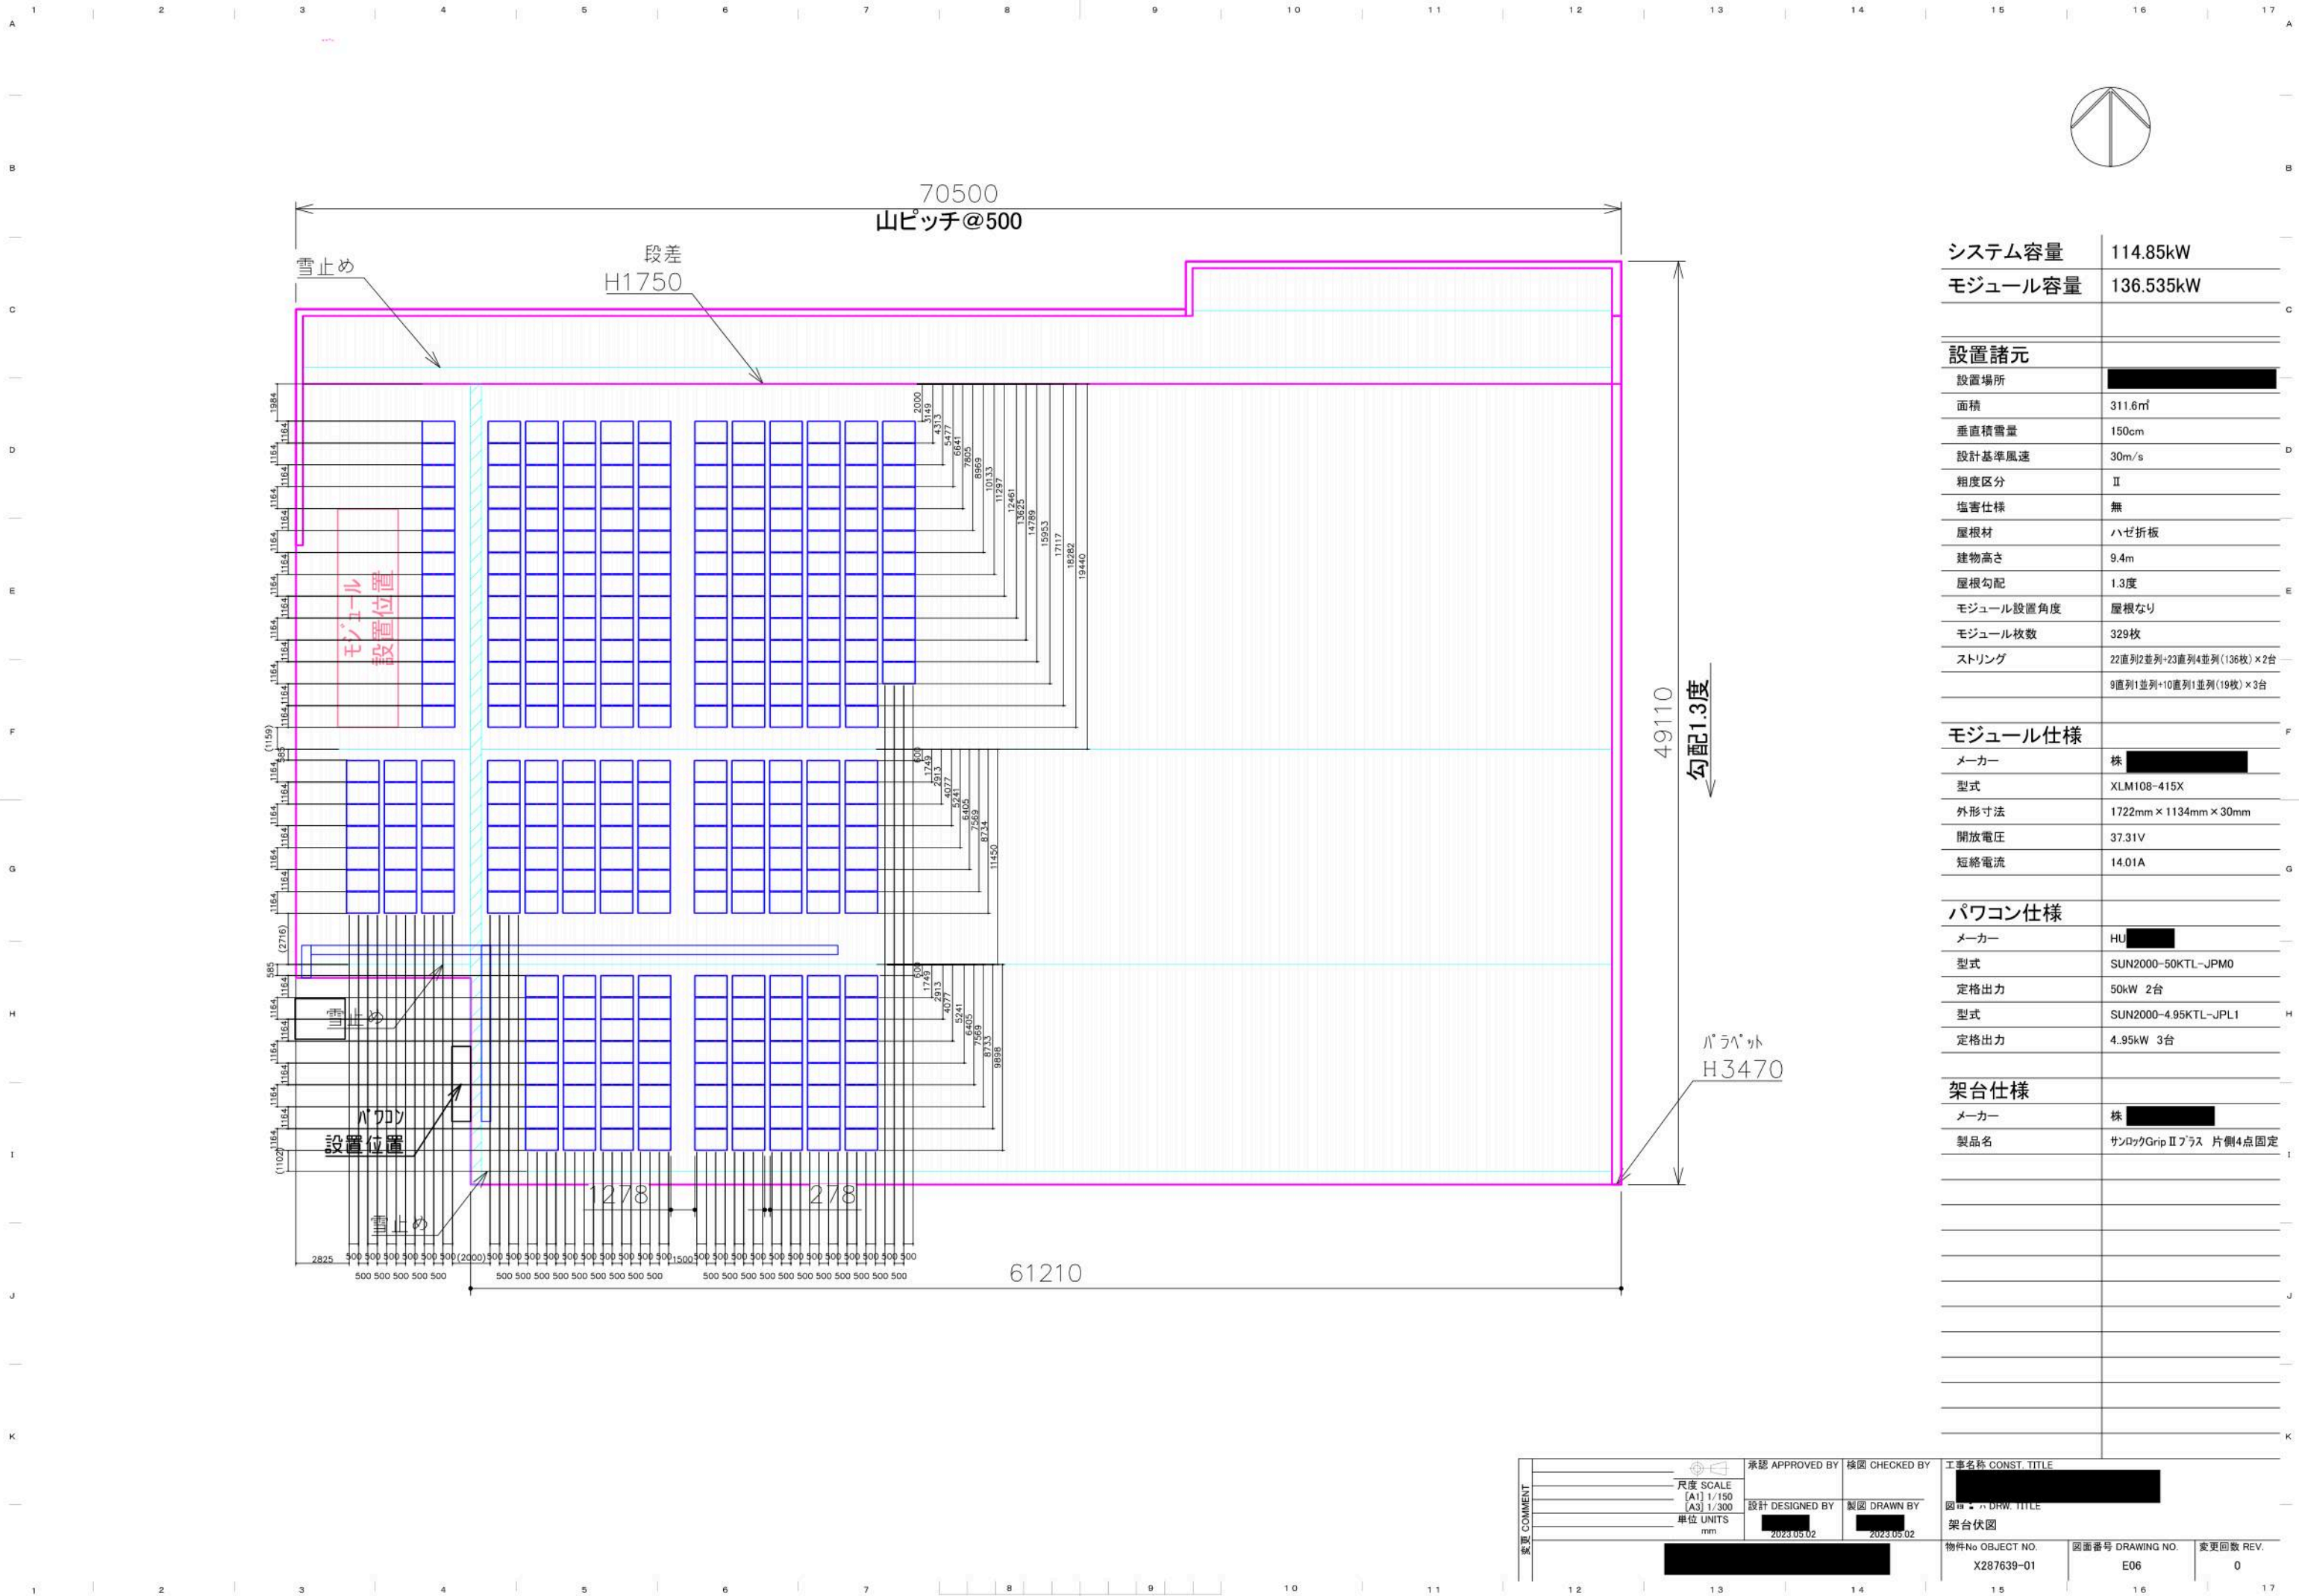

システム容量	114.85kW
モジュール容量	136.535kW

設置諸元	
設置場所	
面積	311.6㎡
垂直積雪量	150cm
設計基準風速	30m/s
粗度区分	Ⅱ
塩害仕様	無
屋根材	ハゼ折板
建物高さ	9.4m
屋根勾配	1.3度
モジュール設置角度	屋根なり
モジュール枚数	329枚
ストリング	22直列2並列+23直列4並列(136枚)×2台 9直列1並列+10直列1並列(19枚)×3台

モジュール仕様	
メーカー	株
型式	XML108-415X
外形寸法	1722mm×1134mm×30mm
開放電圧	37.31V
短絡電流	14.01A

パワコン仕様	
メーカー	HU
型式	SUN2000-50KTL-JPM0
定格出力	50kW 2台
型式	SUN2000-4.95KTL-JPL1
定格出力	4.95kW 3台

架台仕様	
メーカー	株
製品名	サンロックGrip II フラス 片側4点固定

変更 COMMENT	承認 APPROVED BY	校閲 CHECKED BY	工事名称 CONST. TITLE
	設計 DESIGNED BY	製図 DRAWN BY	図面番号 DRW. TITLE
	単位 UNITS	2023.05.02	架台伏図
	mm	2023.05.02	物件No OBJECT NO. X287639-01
			図面番号 DRAWING NO. E06
			変更回数 REV. 0