


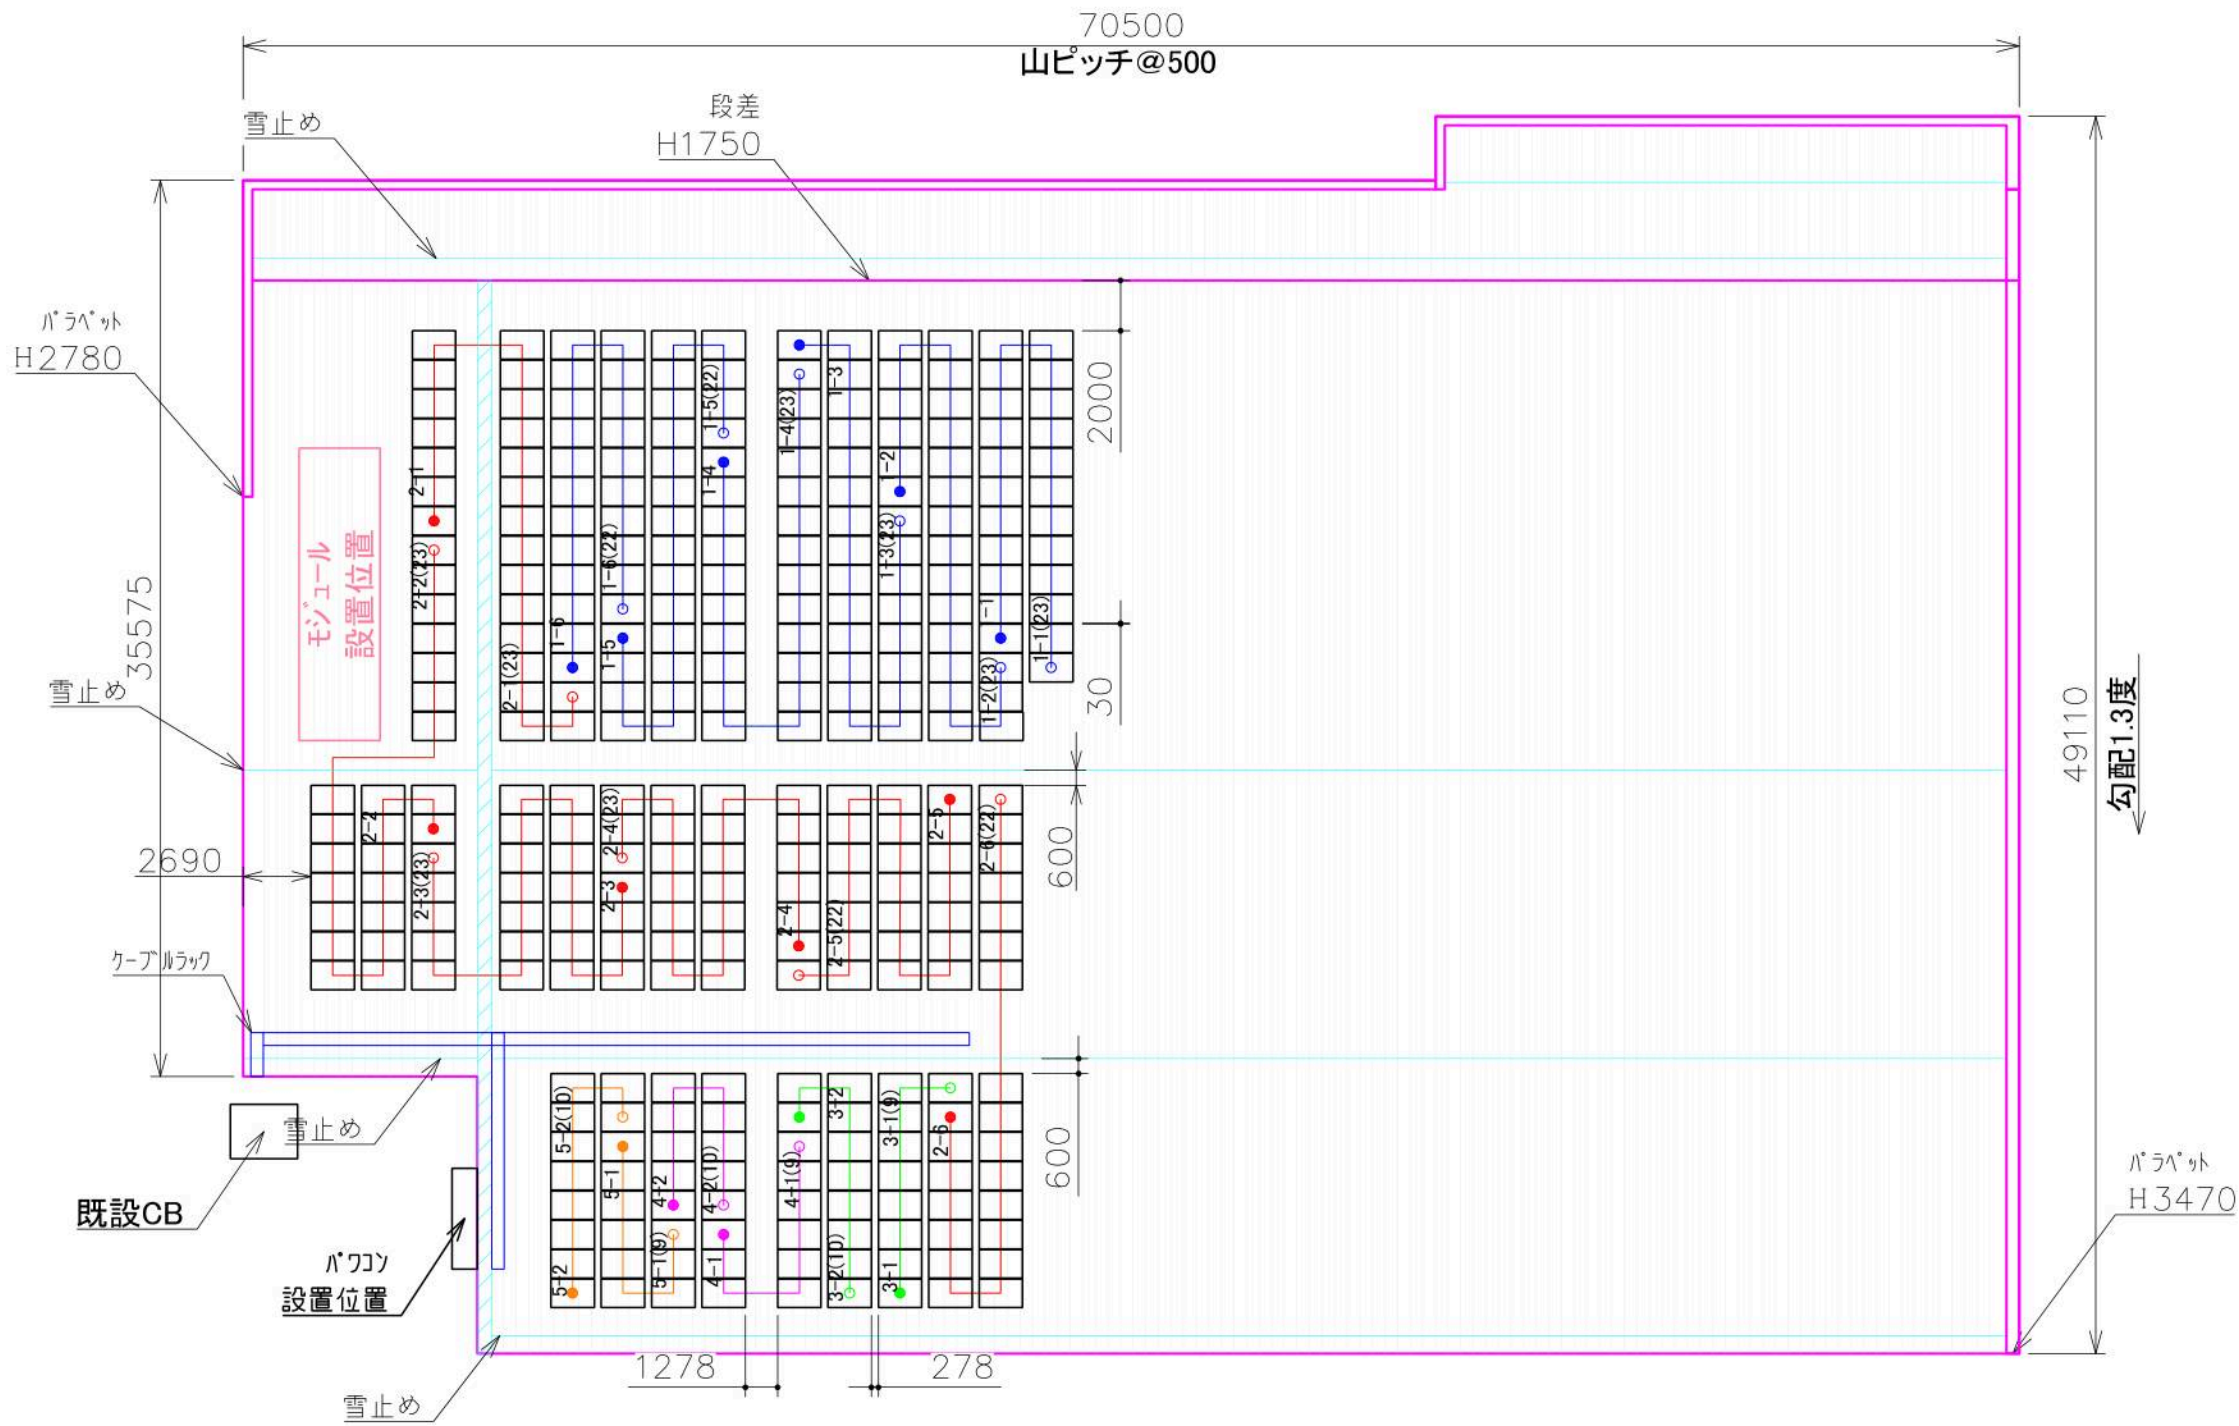

PCS1(50kW)			PCS2(50kW)			PCS3(4.95kW)			PCS4(4.95kW)			PCS5(4.95kW)		
配線No.	線種	長さ	配線No.	線種	長さ	配線No.	線種	長さ	配線No.	線種	長さ	配線No.	線種	長さ
1-1	PVCC5.5SQ	100m	2-1	PVCC5.5SQ	80m	3-1	PVCC5.5SQ	90m	4-1	PVCC5.5SQ	80m	5-1	PVCC5.5SQ	70m
1-2	PVCC5.5SQ	100m	2-2	PVCC5.5SQ	80m	3-2	PVCC5.5SQ	90m	4-2	PVCC5.5SQ	80m	5-2	PVCC5.5SQ	70m
1-3	PVCC5.5SQ	100m	2-3	PVCC5.5SQ	80m									
1-4	PVCC5.5SQ	100m	2-4	PVCC5.5SQ	80m									
1-5	PVCC5.5SQ	100m	2-5	PVCC5.5SQ	80m									
1-6	PVCC5.5SQ	100m	2-6	PVCC5.5SQ	80m									

システム容量	114.85kW
モジュール容量	136.535kW

設置諸元	
設置場所	
面積	311.6㎡
垂直積雪量	150cm
設計基準風速	30m/s
粗度区分	Ⅱ
塩害仕様	無
屋根材	ハゼ折板
建物高さ	9.4m
屋根勾配	1.3度
モジュール設置角度	屋根なり
モジュール枚数	329枚
ストリング	22直列2並列+23直列4並列(136枚)×2台 9直列1並列+10直列1並列(19枚)×3台

モジュール仕様	
メーカー	
型式	XLM108-415X
外形寸法	1722mm×1134mm×30mm
開放電圧	37.31V
短絡電流	14.01A

パワーコン仕様	
メーカー	
型式	SUN2000-50KTL-JPM0
定格出力	50kW 2台
型式	SUN2000-4.95KTL-JPL1
定格出力	4.95kW 3台

架台仕様	
メーカー	
製品名	サンロックGripⅡプラス 片側4点固定

変更 COMMENT	承認 APPROVED BY	検図 CHECKED BY	工事名称 CONST. TITLE
	設計 DESIGNED BY	製図 DRAWN BY	図面名称 DRW. TITLE
	単位 UNITS	mm	ストリング図
	2023.05.02	2023.05.02	物件No OBJECT NO. X287639-01
			図面番号 DRAWING NO. E02
			変更回数 REV. 1