


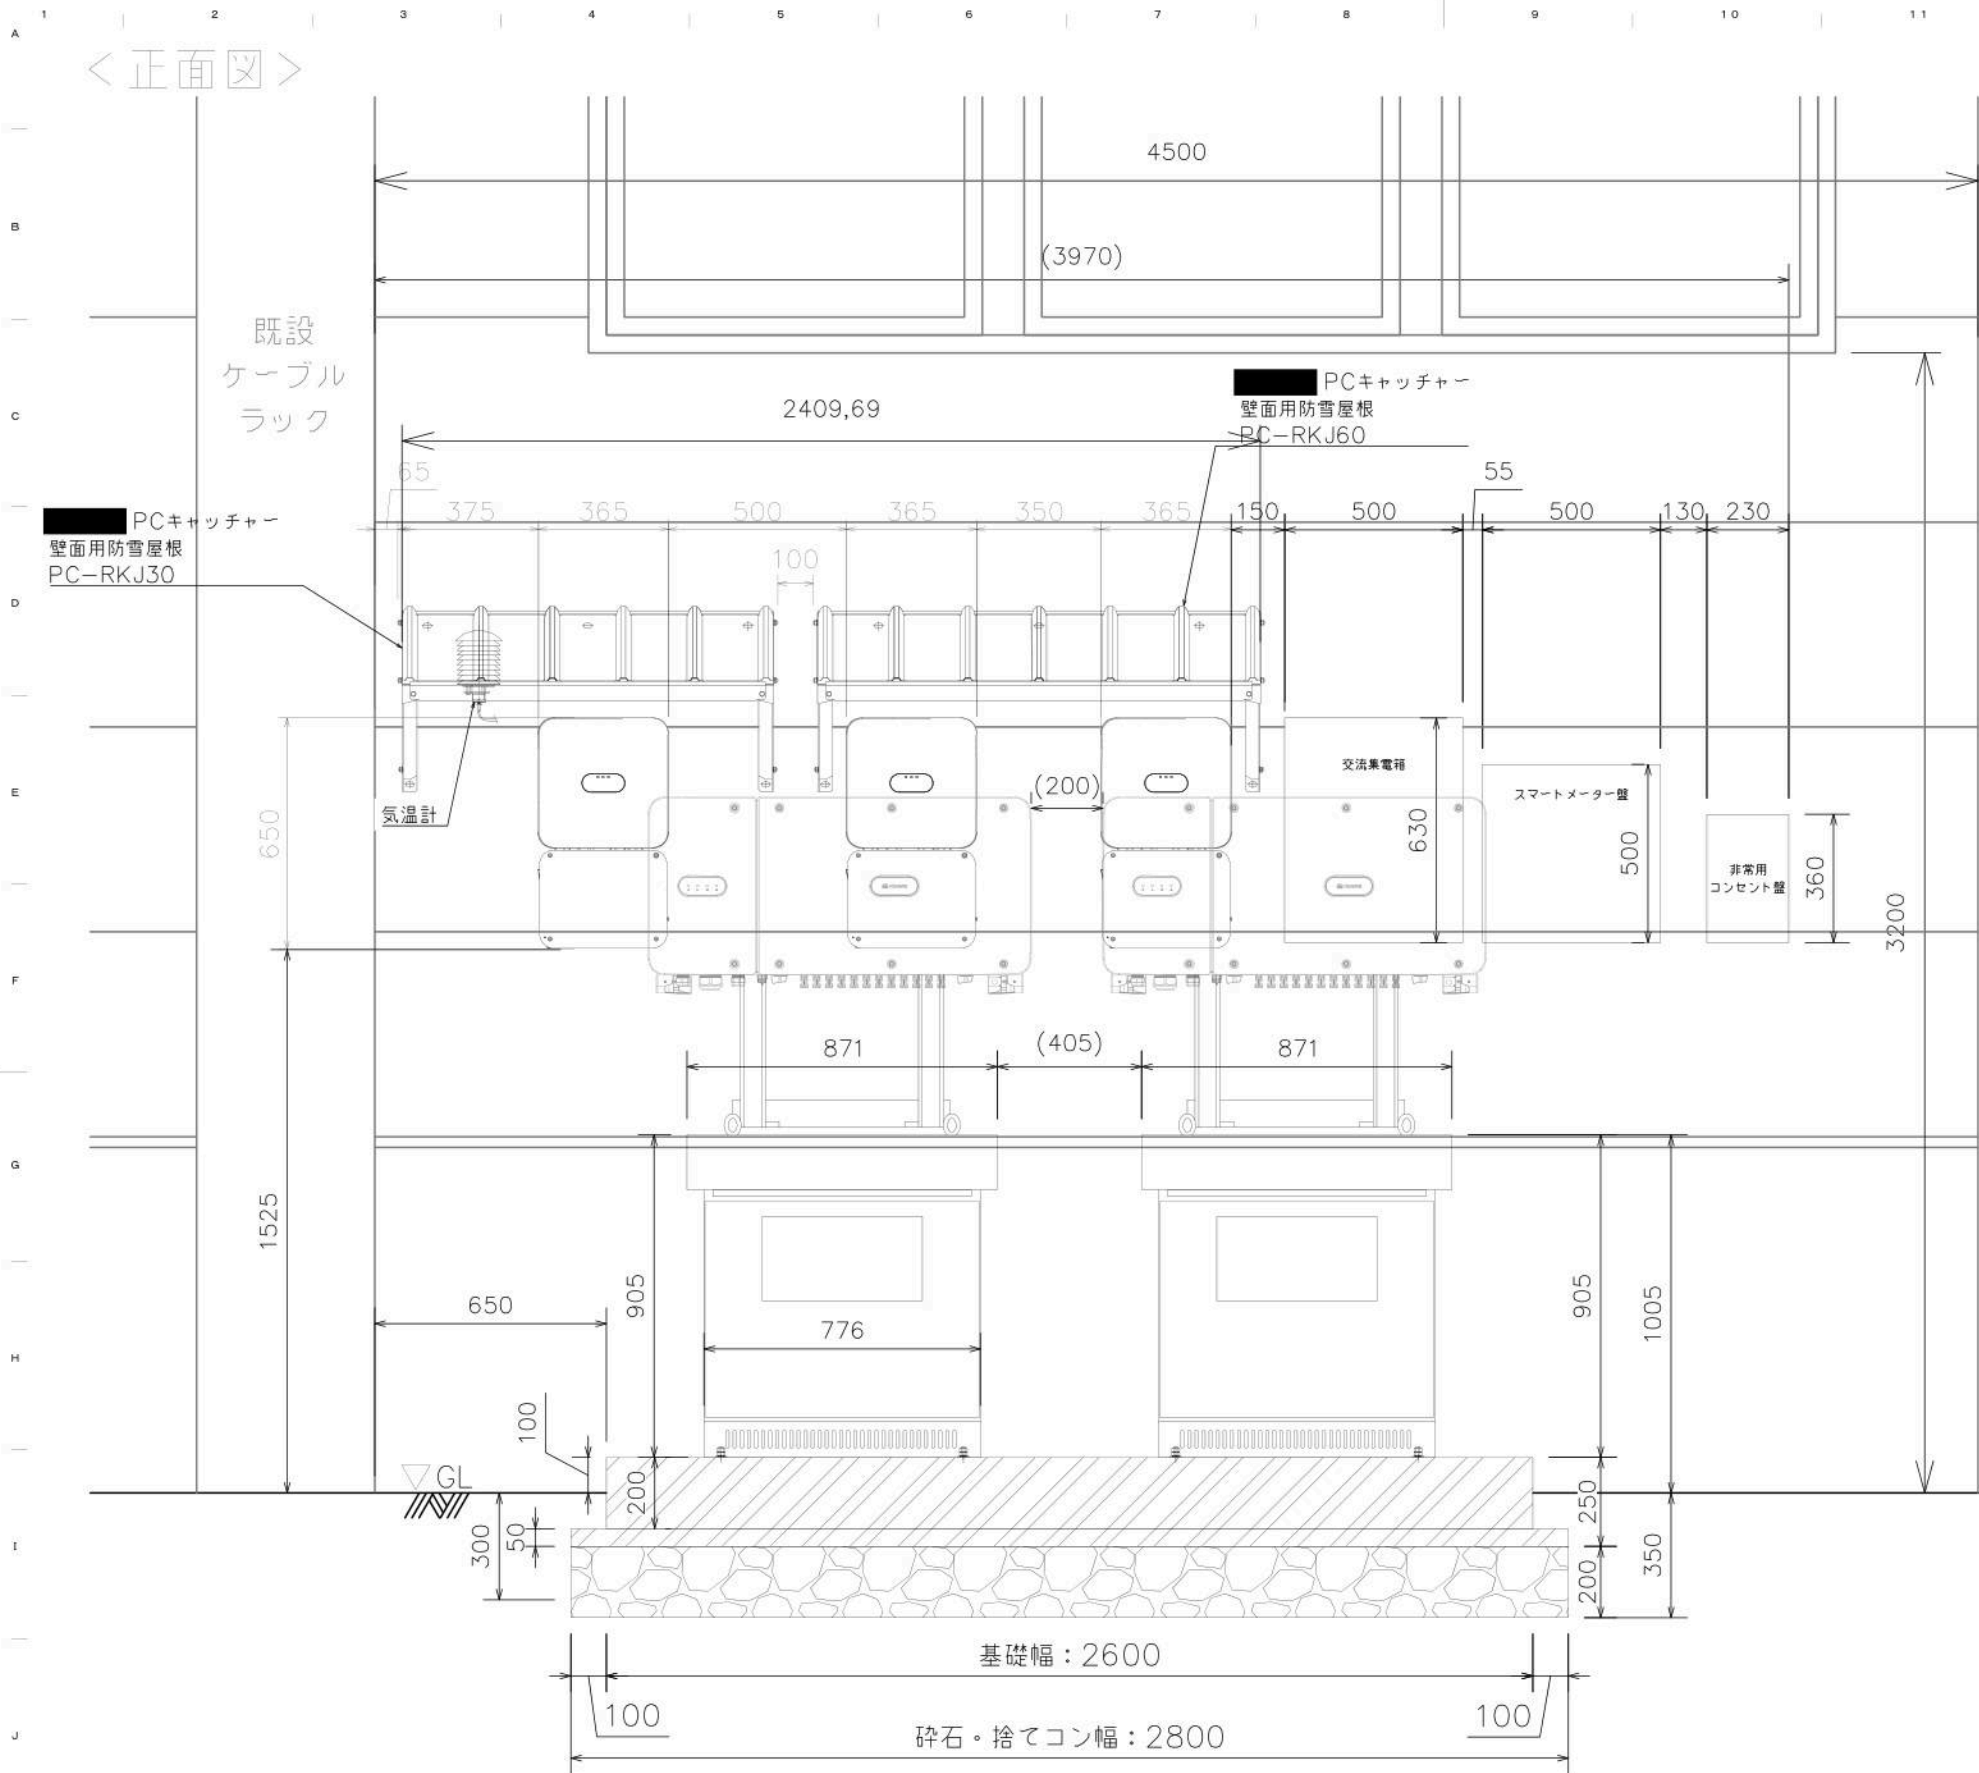

□部材構成

接着系アンカー : M12×4本/台×2台=8本 ※穿孔長：100 mm

コンクリート強度 : $F_c=21\text{N/mm}^2$

コンクリート配合比 : 21-15-20

コンクリート打設量 : W 2.60m×D 1.00m×H 0.20m $\approx 0.70\text{m}^3$

※均しコンクリート込

砕石敷設量 : W 2.80m×D 1.20m×T 0.20m $\approx 0.675\text{m}^3$

型枠面積 : 1.44m^2


掘削土量 : 1.176m^3

鉄筋 : $\phi 6$ #150ワイヤーメッシュ

壁面用防雪屋根 : ■ PC-RKJ30×3基

■ PC-RKJ60×1基

締結用ボルト : M14×5本/台×2台=10本

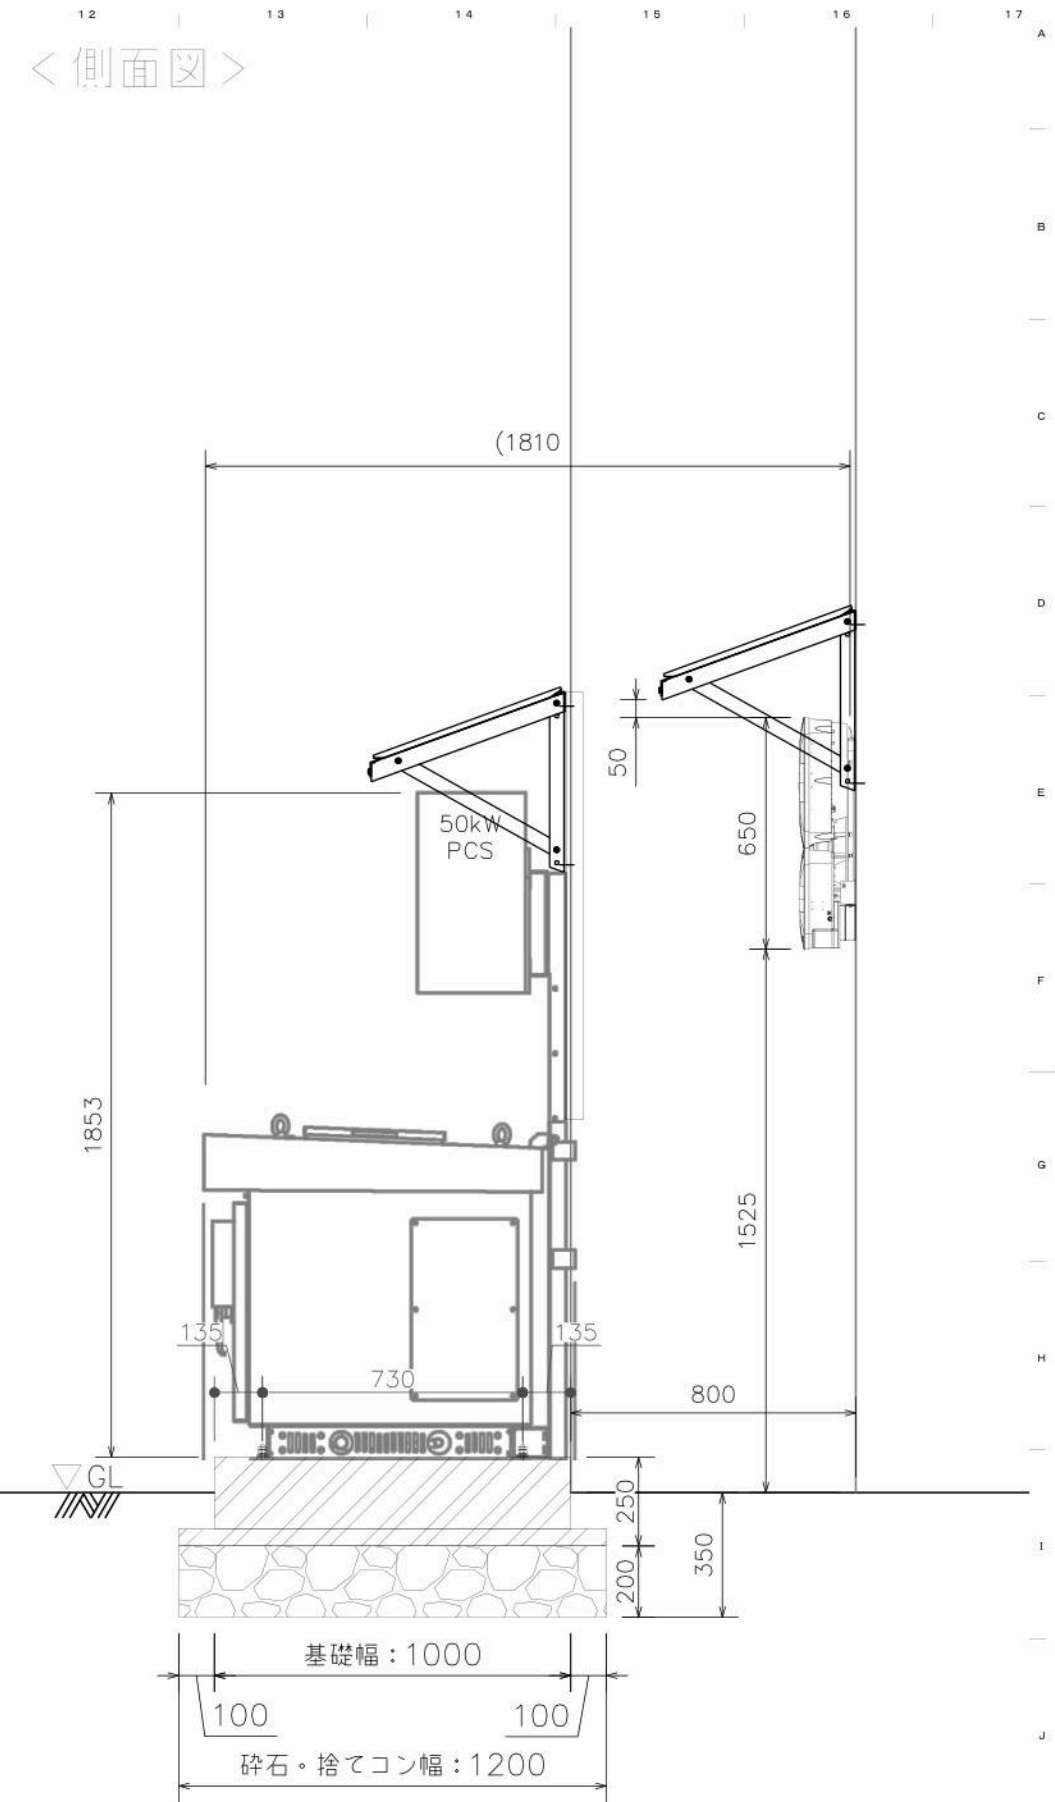

変更 コメント	承認 APPROVED BY	検図 CHECKED BY	工事名称 CONST. TITLE
	尺度 SCALE [A2] 1/15	設計 DESIGNED BY	製図 DRAWN BY
	単位 UNITS mm	2 8	2 8
	図面名称 DRW. TITLE	物件No OBJECT NO.	図面番号 DRAWING NO.
		X287639-01	E01
			変更回数 REV.
			2